



SERA-CTRL-01 - Schema Electrica de Cablare - 12V DC + UPS Solar

TR1 230V/12V | Panou Solar 100W | MPPT 10A | Acumulator 12V 60Ah | M1/M2 12V 5A | ESP32 | K1-K5 Relee 12V

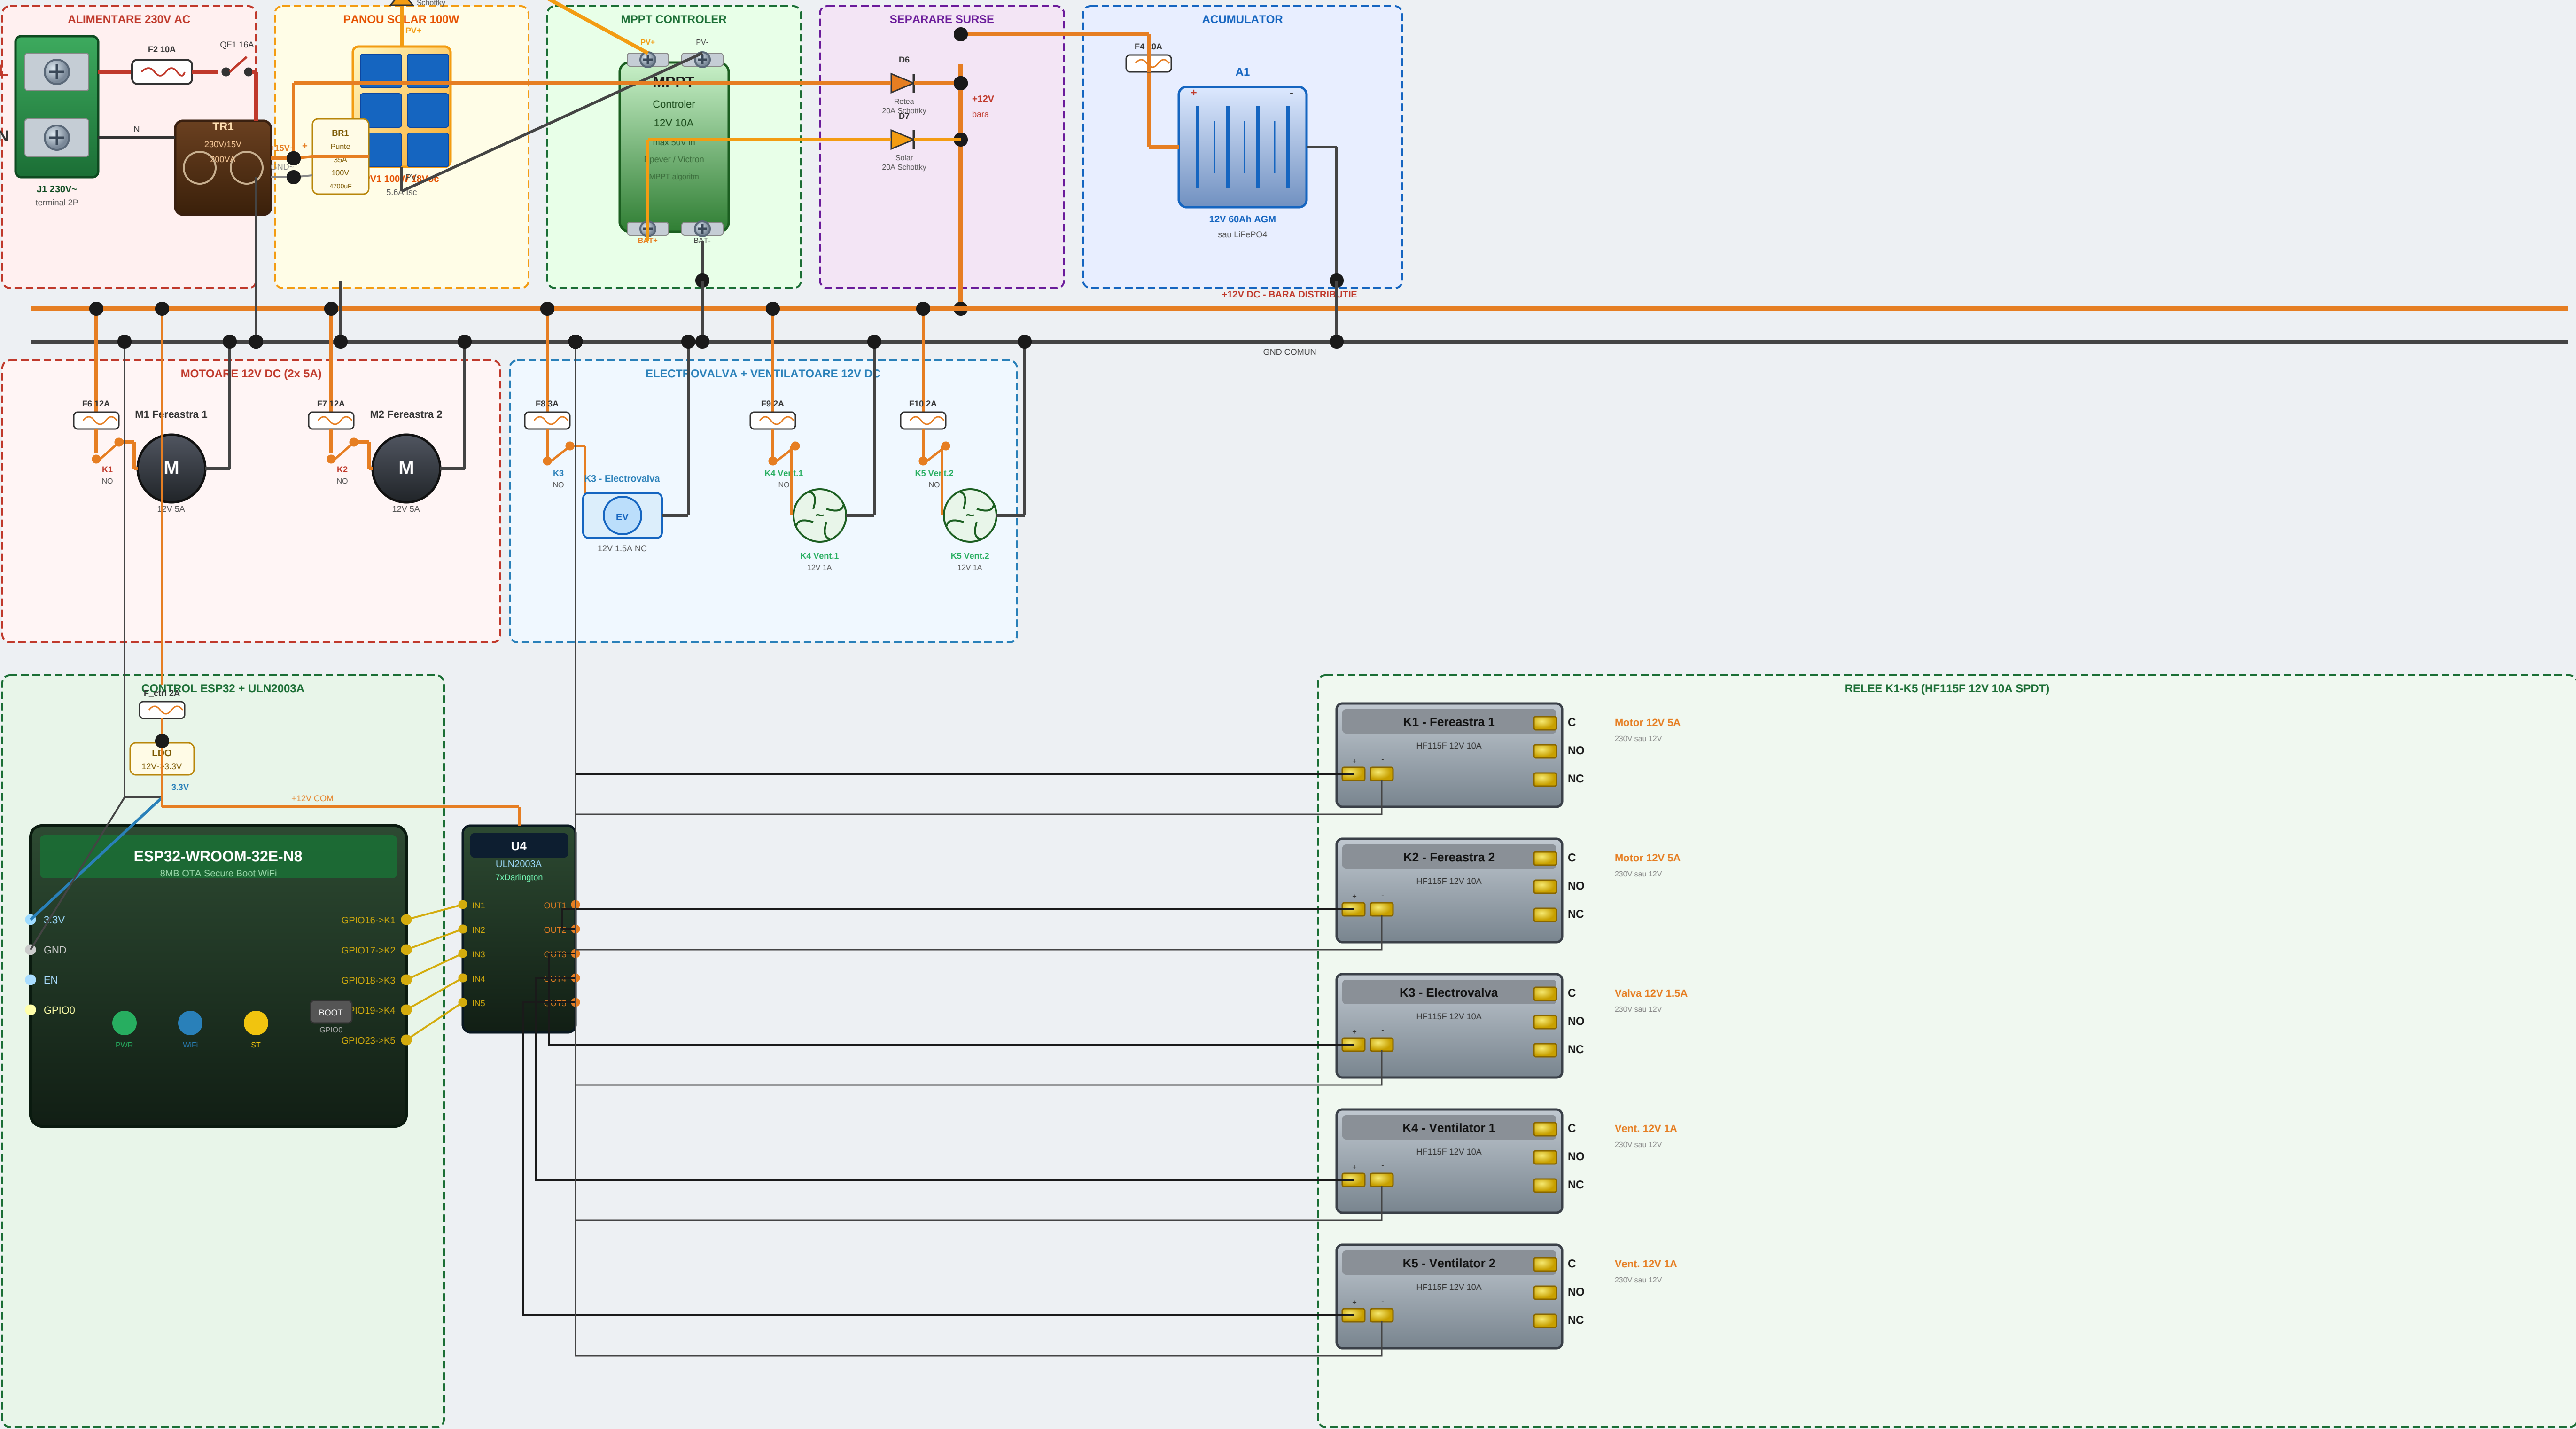

SENZORI I/O si LEGENDA

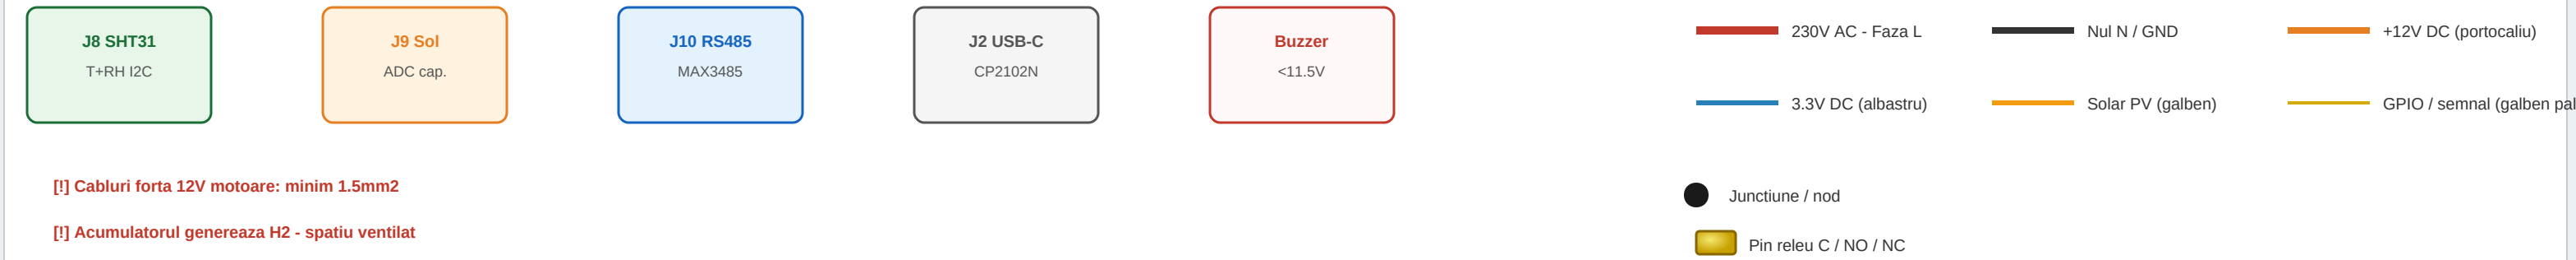

[1] Cabluri forta 12V motoare: minim 1.5mm2

[2] Acumulatorul genereaza H2 - spatiu ventilat

[3] 230V AC: instalare EXCLUSIV de electrician autorizat